



VICINITY MAP NOT TO SCALE

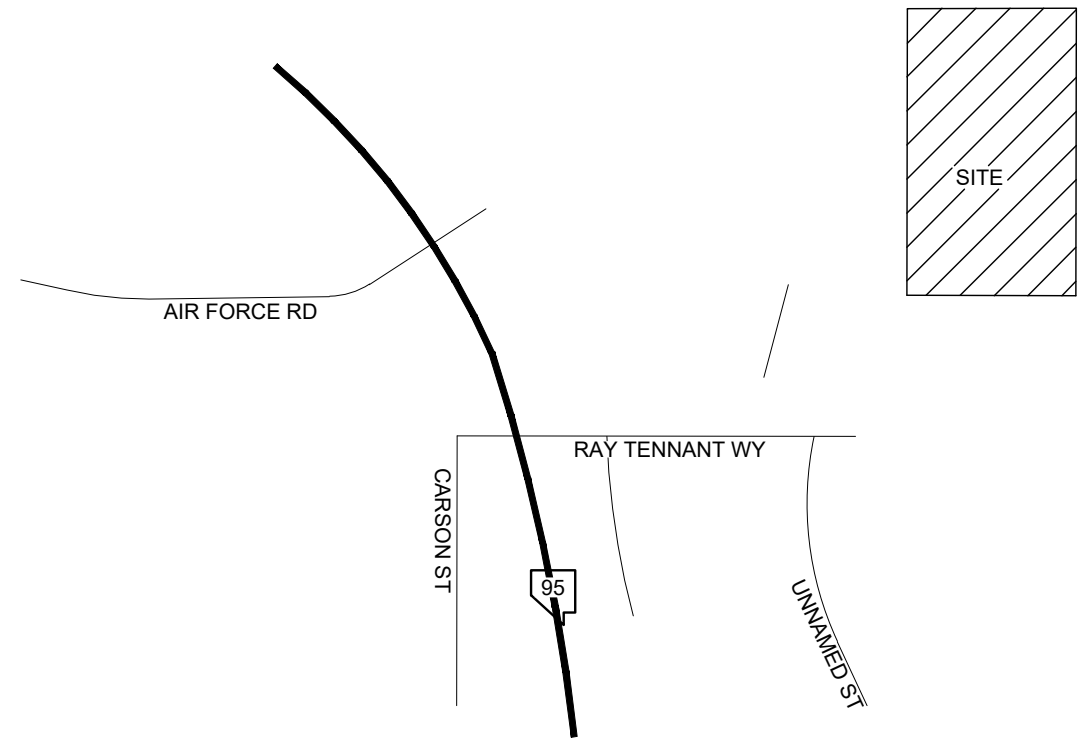

SITE MAP NOT TO SCALE

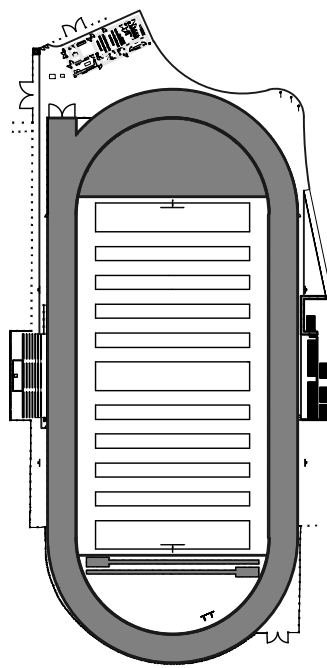

LEGEND

	EXISTING	PROPOSED
PROJECT BOUNDARY	---	---
RIGHT-OF-WAY	---	---
CENTERLINE	---	---
PROPERTY LINE	---	---
EDGE OF PAVEMENT	---	---
SIDEWALK	---	---
CURB AND GUTTER	---	---
FENCE	---	---
CONTOUR (1' INTERVAL)	---	---
CONTOUR (5' INTERVAL)	---	---
DIRECTION OF FLOW	---	---
CUT LINE-ASPHALT	---	---
SCARP (SLOPE VARIES)	---	---
DESIGN ELEVATION	(10.00)	10.00
FUTURE ELEVATION		[10.00]
NUMBER OF RETAINING COURSES		
RETAINING WALL	---	---
CMU WALL	---	---
SOLID GROUTED WALL - NO RETAINING	---	---
CUT-OFF WALL	---	---
POWER POLE	---	---
SIDEWALK RAMP	---	---
CURB DROP INLET	---	---
STORM DRAIN W/IN-HOLE	---	---
CUT-FILL LINE	---	---
SIGHT VISIBILITY ZONE	---	---
CAP & 2" BLOW OFF VALVE	---	---
WATERLINE FITTINGS	---	---
GATE VALVE	---	---
FIRE HYDRANT	---	---
SEWER LINE W/IN-HOLE	---	---
SEWER LATERAL	---	---
WATER LINE	---	---
WATER LATERAL W/ METER	---	---
PRESSURE REDUCING VALVE	---	---
BACKWATER VALVE	---	---
200A SERVICE PEDESTAL	---	---
STREET LIGHT CONDUIT	---	---
F.A.S.T. CONDUIT	---	---
TRAFFIC SIGN	---	---
STOP SIGN W/ STREET NAME SIGN	---	---
LED LUMINAIRE W/ POLE (RESIDENTIAL)	---	---
LED LUMINAIRE W/ POLE (ARTERIAL)	---	---
LED LUMINAIRE W/ POLE (INTERSECTION)	---	---

ABBREVIATIONS

AC	ASPHALTIC CONCRETE	LWVO	LAS VEGAS VALLEY WATER DISTRICT
ACP	ASBESTOS CEMENT PIPE	MAX	MAXIMUM
AVE	AVENUE	MH	MANHOLE
BC	BACK OF CURB	MIN	MINIMUM
BCR	BACK OF CURB RADIUS	NO	NUMBER
BFE	BASE FLOOD ELEVATION	NTS	NOT TO SCALE
BFP	BACK FLOW PREVENTOR	OC	ON CENTER
BLM	BUREAU OF LAND MANAGEMENT	PB	PULL BOX
BM	BENCH MARK	PC	POINT OF CURVE
BO	BOUNDARY	PCC	POINT OF COMPOUND CURVE
BRPM	BLUE RAISED PAVEMENT MARKER	PE	POLYETHYLENE
BVC	BEGIN VERTICAL CURVE	PI	POINT OF INTERSECTION
BW	BOTTOM OF WALL	PL	PROPERTY LINE
CATV	CABLE TELEVISION	PLT	PLATE
CC	CLARK COUNTY	POC	POINT OF CONNECTION
CCAUSS	CLARK COUNTY AREA UNIFORM STANDARD DRAWING	PP	POWER POLE
CCFD	CLARK COUNTY FIRE DEPARTMENT	P&P	PLAN AND PROFILE
CCWRD	CLARK COUNTY WATER RECLAMATION DISTRICT	PRC	POINT OF REVERSE CURVE
CL	CENTERLINE	PROJ	PROJECT
CLSM	CONTROLLED LOW STRENGTH MATERIAL	PRV	PRESSURE REDUCING VALVE
CLV	CITY OF LAS VEGAS	PT	POINT OF TANGENCY
CMP	CORRUGATED METAL PIPE	PVC	POLYVINYL CHLORIDE
CNLV	CITY OF NORTH LAS VEGAS	R	RADIUS
CO	CLEAN OUT, SEWER	RCB	REINFORCED CONCRETE BOX
COH	CITY OF HENDERSON	RCP	REINFORCED CONCRETE PIPE
CY	CUBIC YARD	RW	RIGHT-OF-WAY
DCSWCS	DESIGN AND CONSTRUCTION STANDARDS FOR WASTE WATER COLLECTION SYSTEMS	RT	RIGHT
DI	DROP INLET	SD	STORM DRAIN
DIP	DUCTILE IRON PIPE	SHT	SHEET
DR	DRIVE	STLT	STREETLIGHT
EASE	EASEMENT	SNWA	SOUTHERN NEVADA WATER AUTHORITY
EC	END OF CURVE	SS	SANITARY SEWER
EG	EXISTING GRADE	ST	STREET
ELEC	ELECTRICAL	STA	STATION
EP	EDGE OF PAVEMENT	STD	STANDARD
EVC	END VERTICAL CURVE	SVZ	SIGHT VISIBILITY ZONE
EX	EXISTING	SW	SIDEWALK
FF	FINISH FLOOR ELEVATION	SY	SQUARE YARD
FG	FINISH GRADE	TC	TOP OF CURB
FH	FIRE HYDRANT	TCD	TRAFFIC CONTROL DEVICE
FL	FLOW LINE	TELE	TELEPHONE
FT	FEET	TF	TOP OF FOOTING
G	GRADING	T.O.P.	TOP OF PIPE
GB	GRADE BREAK	TR	TOP OF RETAINING
OFF	GARAGE FINISH FLOOR	TW	TOP OF WALL
HP	HIGH POINT	TYP	TYPICAL
HPS	HIGH PRESSURE GAS	UDACS	UNIFORM DESIGN AND CONSTRUCTION STANDARDS
INV	INVERT	UT	UTILITY
LF	LINEAR FEET	VC	VERTICAL CURVE
LN	LANE	VCP	VITRIFIED CLAY PIPE
LS	LANDSCAPE	VG	VALLEY GUTTER
LT	LEFT	W	WATER
		ZC	ZERO LIP CURB

CONSTRUCTION ACCESS POINT
THE DESIGNATED CONSTRUCTION ACCESS POINT SHALL BE XXXXXX.

Avoid overhead power line contact. It's costly.

Call before you Overhead
1-702-227-2929

Avoid cutting underground utility lines. It's costly.

Call before you Dig
CALL
811
OR
1-800-642-2444

Sheet List Table

Sheet Number	Sheet Title	Sheet Description
01	C1	COVER
02	C2	GENERAL NOTES
03	MG	MASTER GRADING
04	G1	GRADING PLAN 1
05	G2	GRADING PLAN 2
06	GD	GRADING DETAILS

ENGINEER
TANEY ENGINEERING
6030 SOUTH JONES BLVD
LAS VEGAS, NV 89118
(702) 362-8844 PHONE (702) 362-5233 FAX

OWNER
NYE COUNTY SCHOOL DISTRICT
7250 PEAK DRIVE, SUITE 216
TONOPAH, NV, 89149-0113

DEVELOPER
CICELY STEWART
KNIT DESIGNING COMMUNITIES
7250 PEAK DRIVE, SUITE 216
LAS VEGAS, NV 89128
(702) 363-2222
CICELYS@KNITSTUDIOS.COM

UTILITY DISCLAIMER
EXISTING UTILITY LOCATIONS SHOWN HEREIN ARE APPROXIMATE ONLY. IT SHALL BE THE CONTRACTORS RESPONSIBILITY TO DETERMINE THE EXACT VERTICAL AND HORIZONTAL LOCATION OF ALL EXISTING UNDERGROUND UTILITIES PRIOR TO COMMENCING CONSTRUCTION. NO REPRESENTATION IS MADE THAT ALL EXISTING UTILITIES ARE SHOWN HEREON. THE ENGINEER ASSUMES NO RESPONSIBILITY FOR UTILITIES NOT SHOWN OR UTILITIES NOT SHOWN IN THEIR EXISTING LOCATIONS.

BASIS OF BEARING
SOUTH 20°11'12" EAST.
BEING THE GEODETIC BEARING FROM NDOT POINT 1252106 TO POINT 125105, NEVADA SPC, CENTRAL ZONE. COORDINATES WERE OBTAINED FROM THE NDOT SURVEY MONUMENT CORCL REPORT, LPN 1440, 05-07-2022.

BENCHMARK
NDOT SURVEY CONTROL MONUMENT
1252106
FOUND 0.17" BRASS CAP IN FENO ON POLYROCK & STAMPED "1252106M 2012". TO REACH STATION GO TO US 95 MILEPOST NY 107.75. THE STATION IS 45' WEST OF THE WEO OF SOUTHBOUND US 95 AN D110' SOUTH OF THE "SCOLARIX" SIGN. AN ORANGE CARSONITE WITNESS POST IN SET 3' WEST OF STATION.
ELEVATION 6204.14 (NAVD 88)

LEGAL DESCRIPTION
THE SOUTHWEST QUARTER (SW 1/4) OF THE NORTHEAST QUARTER (NE 1/4) AND A PORTION OF THE EAST HALF (E 1/2) OF THE SOUTHEAST QUARTER (SE 1/4) OF THE NORTHWEST QUARTER (NW 1/4) OF SECTION 1, TOWNSHIP 2 NORTH, RANGE 42, M.D.M., NYE COUNTY, NEVADA.


TONOPAH HS FOOTBALL FIELD

FIELD REPLACEMENT

IMPROVEMENT PLANS


NYE COUNTY, NEVADA

KNIT DESIGNING COMMUNITY

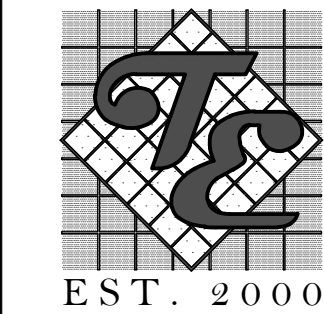






TANEY ENGINEERING
CIVIL ENGINEERING & LAND SURVEYING
6030 S. JONES BLVD
LAS VEGAS, NV 89118
(702) 362-8844
INFO@TANEYCORP.COM

TONOPAH HS FOOTBALL FIELD
FOOTBALL FIELD
NYE COUNTY SCHOOL DISTRICT

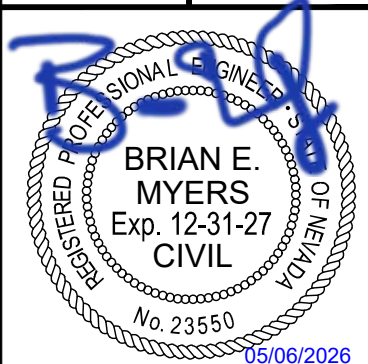

Brian Myers
Digitaly signed by Brian Myers
Date: 2026.05.06 11:40:11-07'07

DATE:	5/6/2026
SCALE:	----
JOB NO:	KNC-24-009
DESIGNED BY:	BSI
CHECKED BY:	BM
SHEET NAME:	C1
SHEET NUMBER:	01 OF 09
NYE	00000000

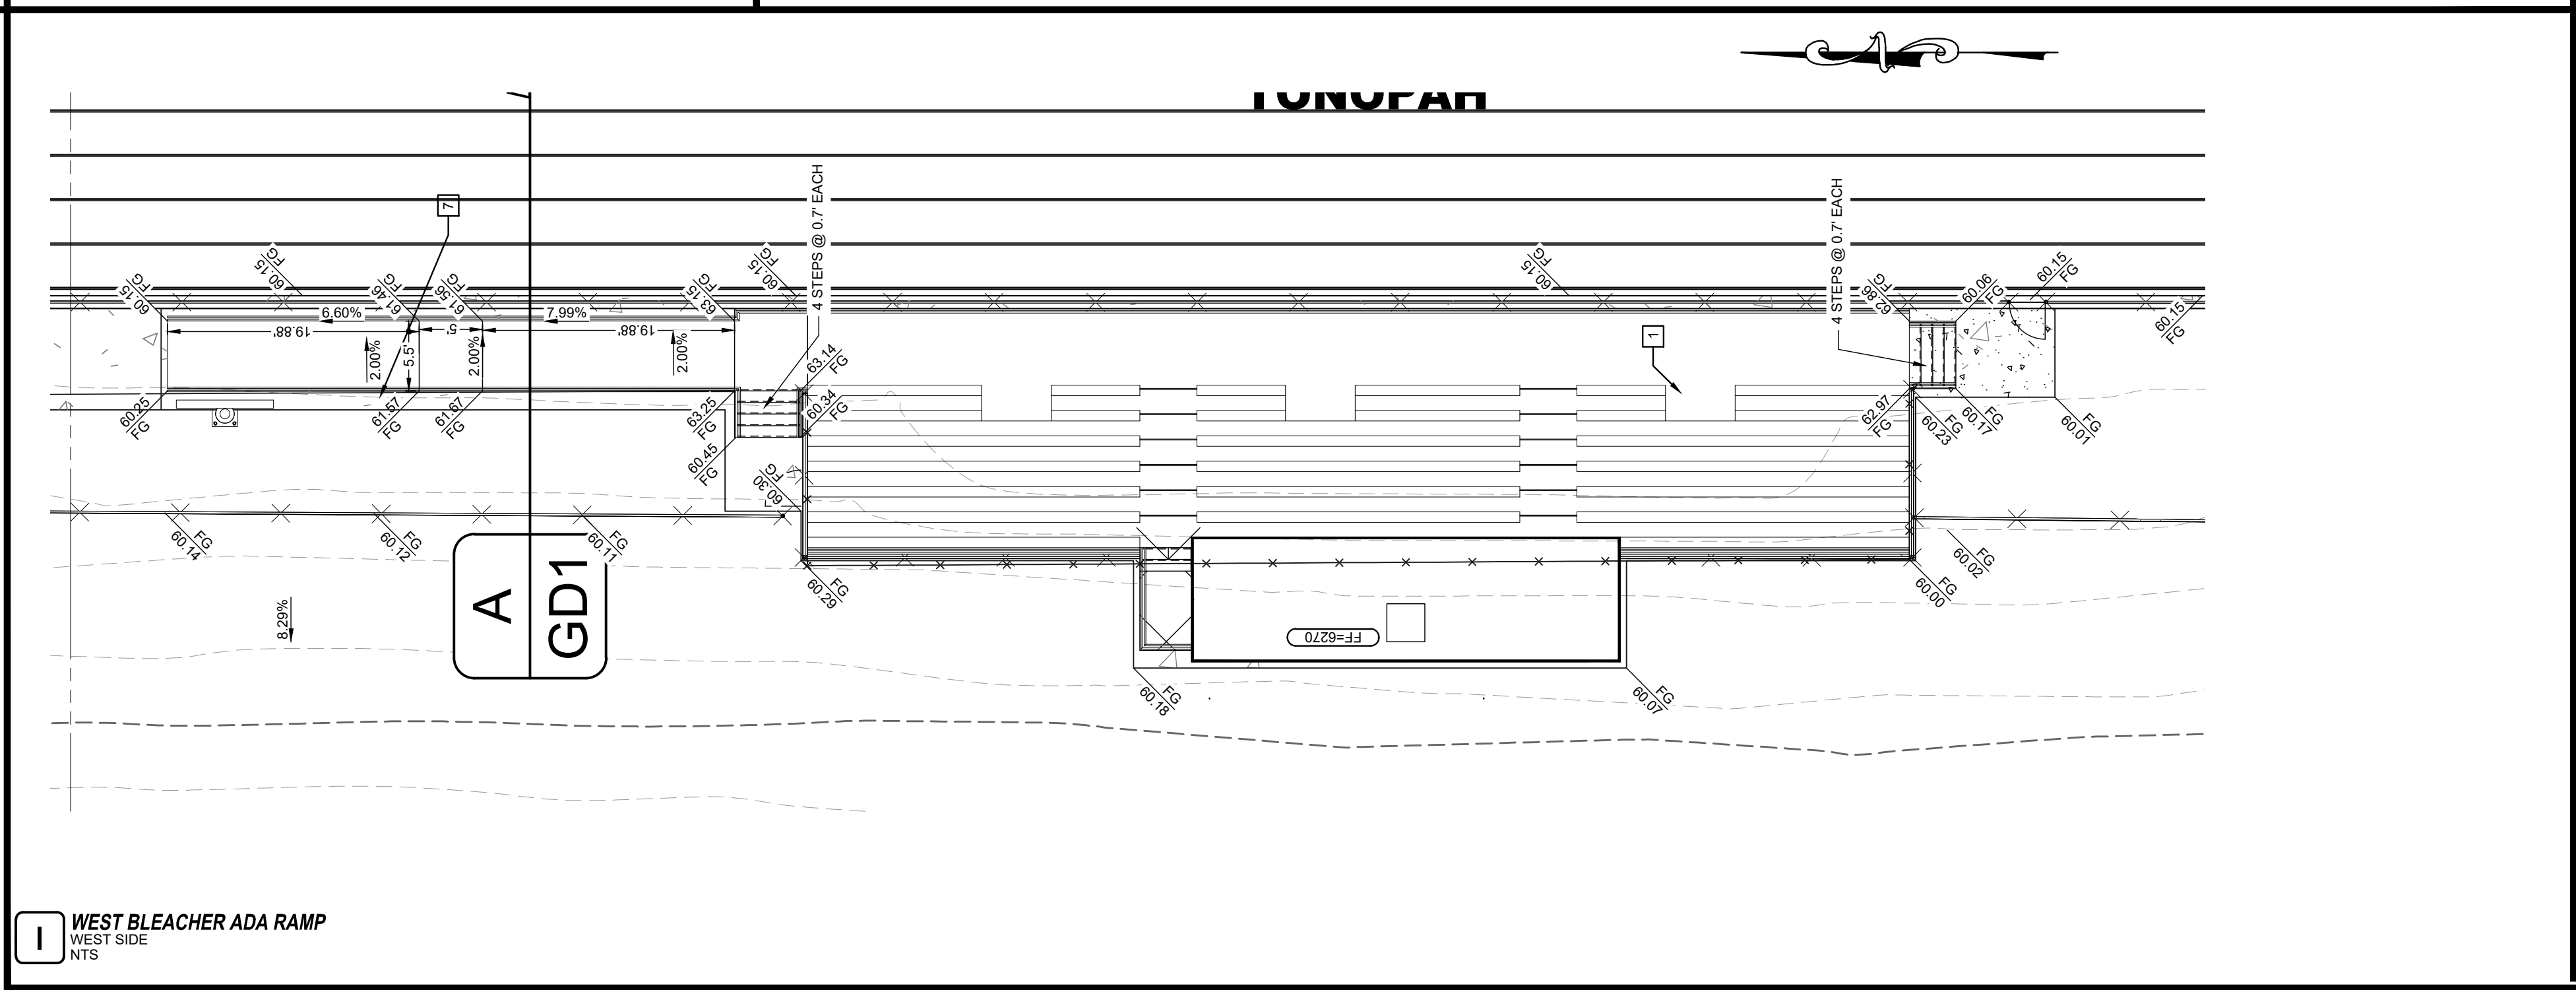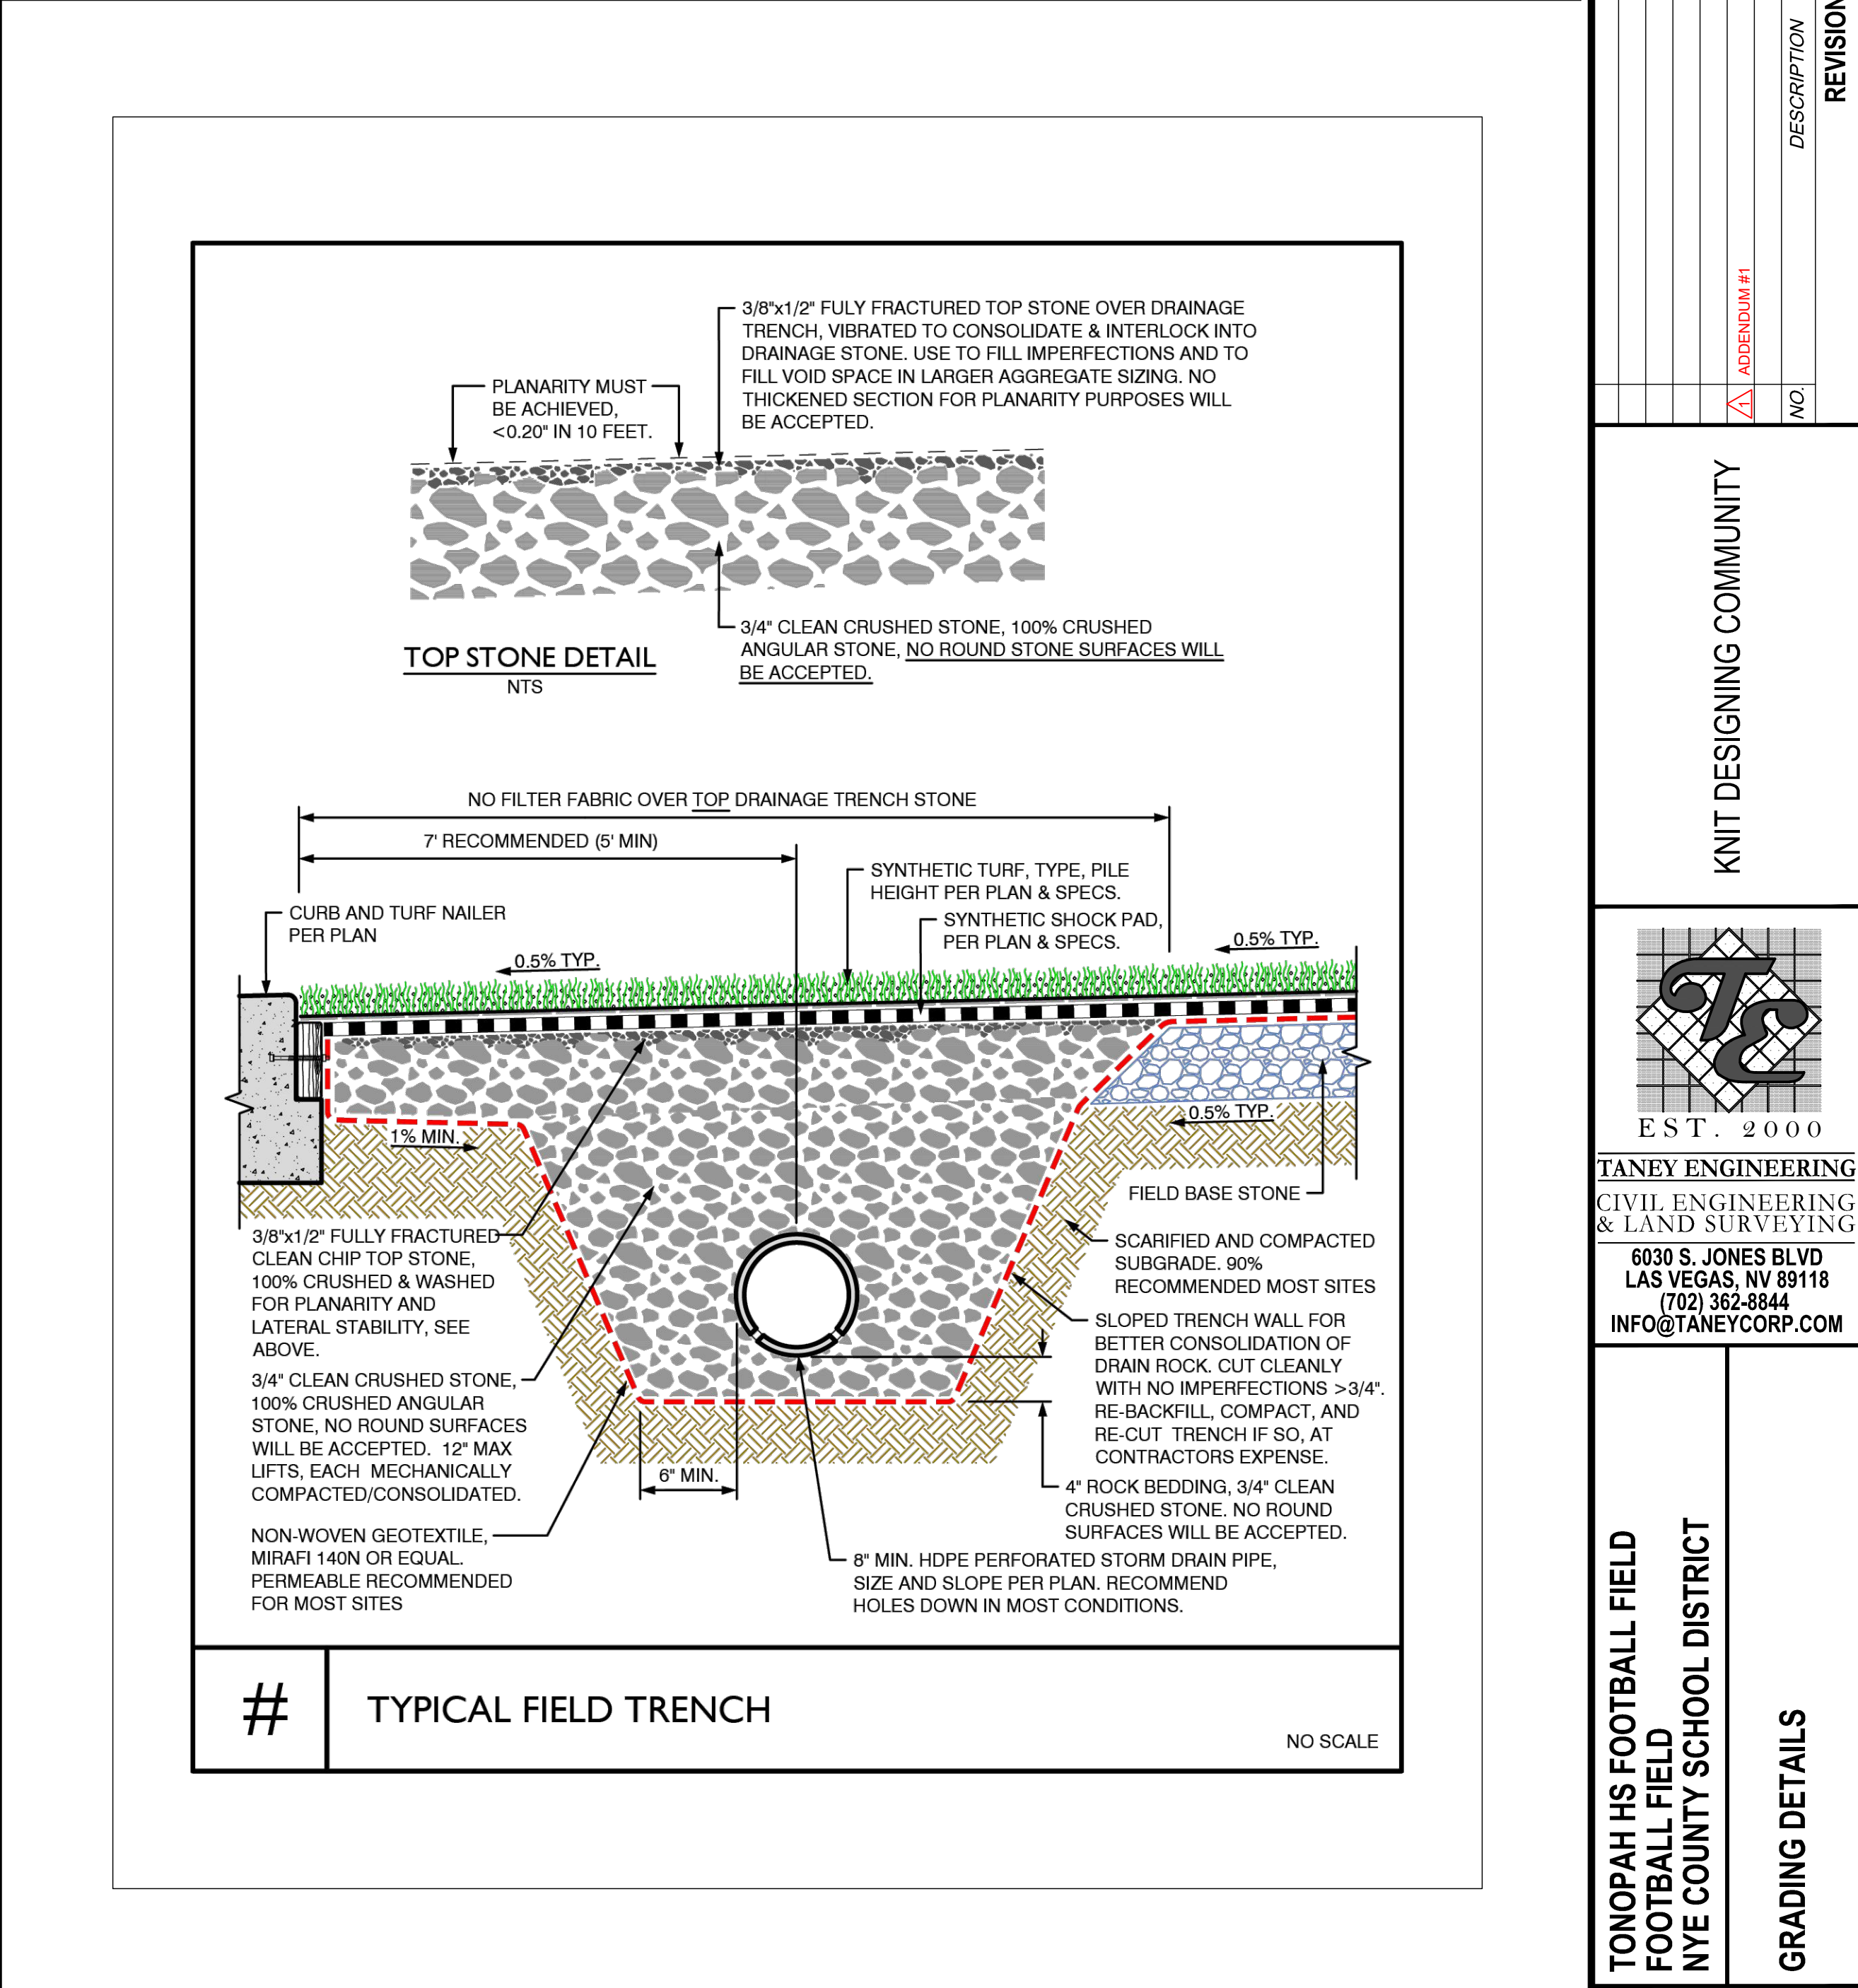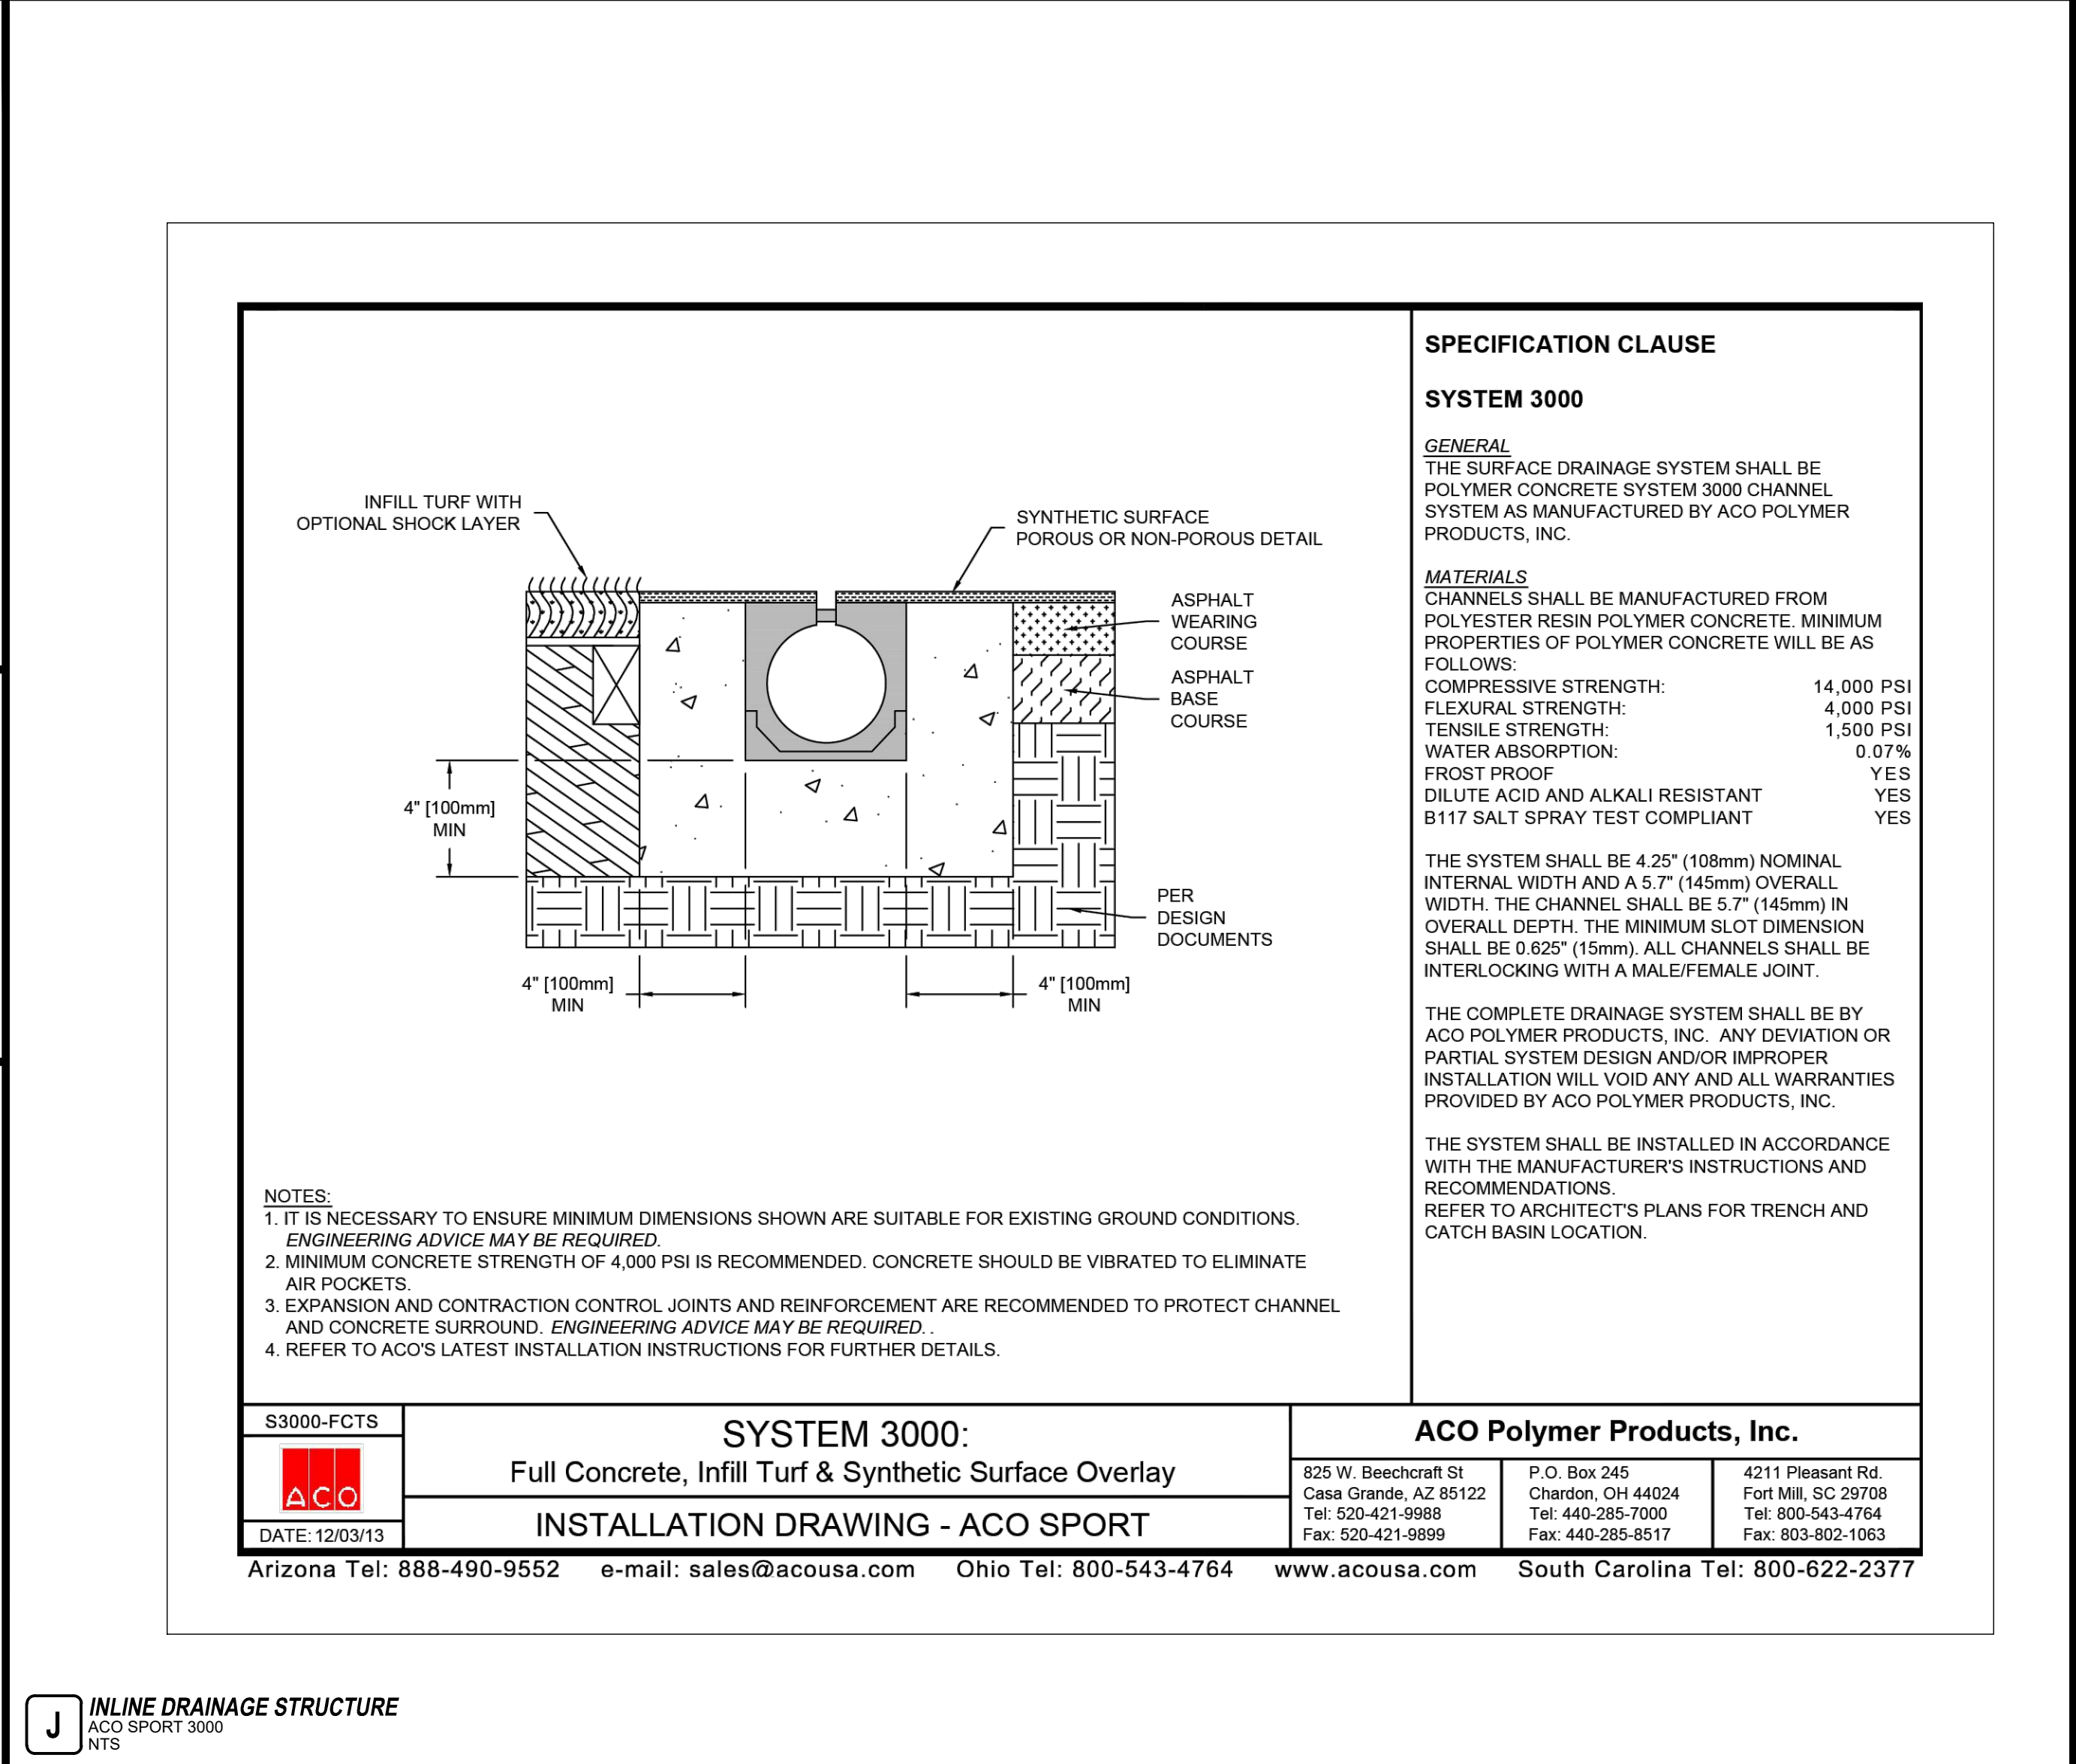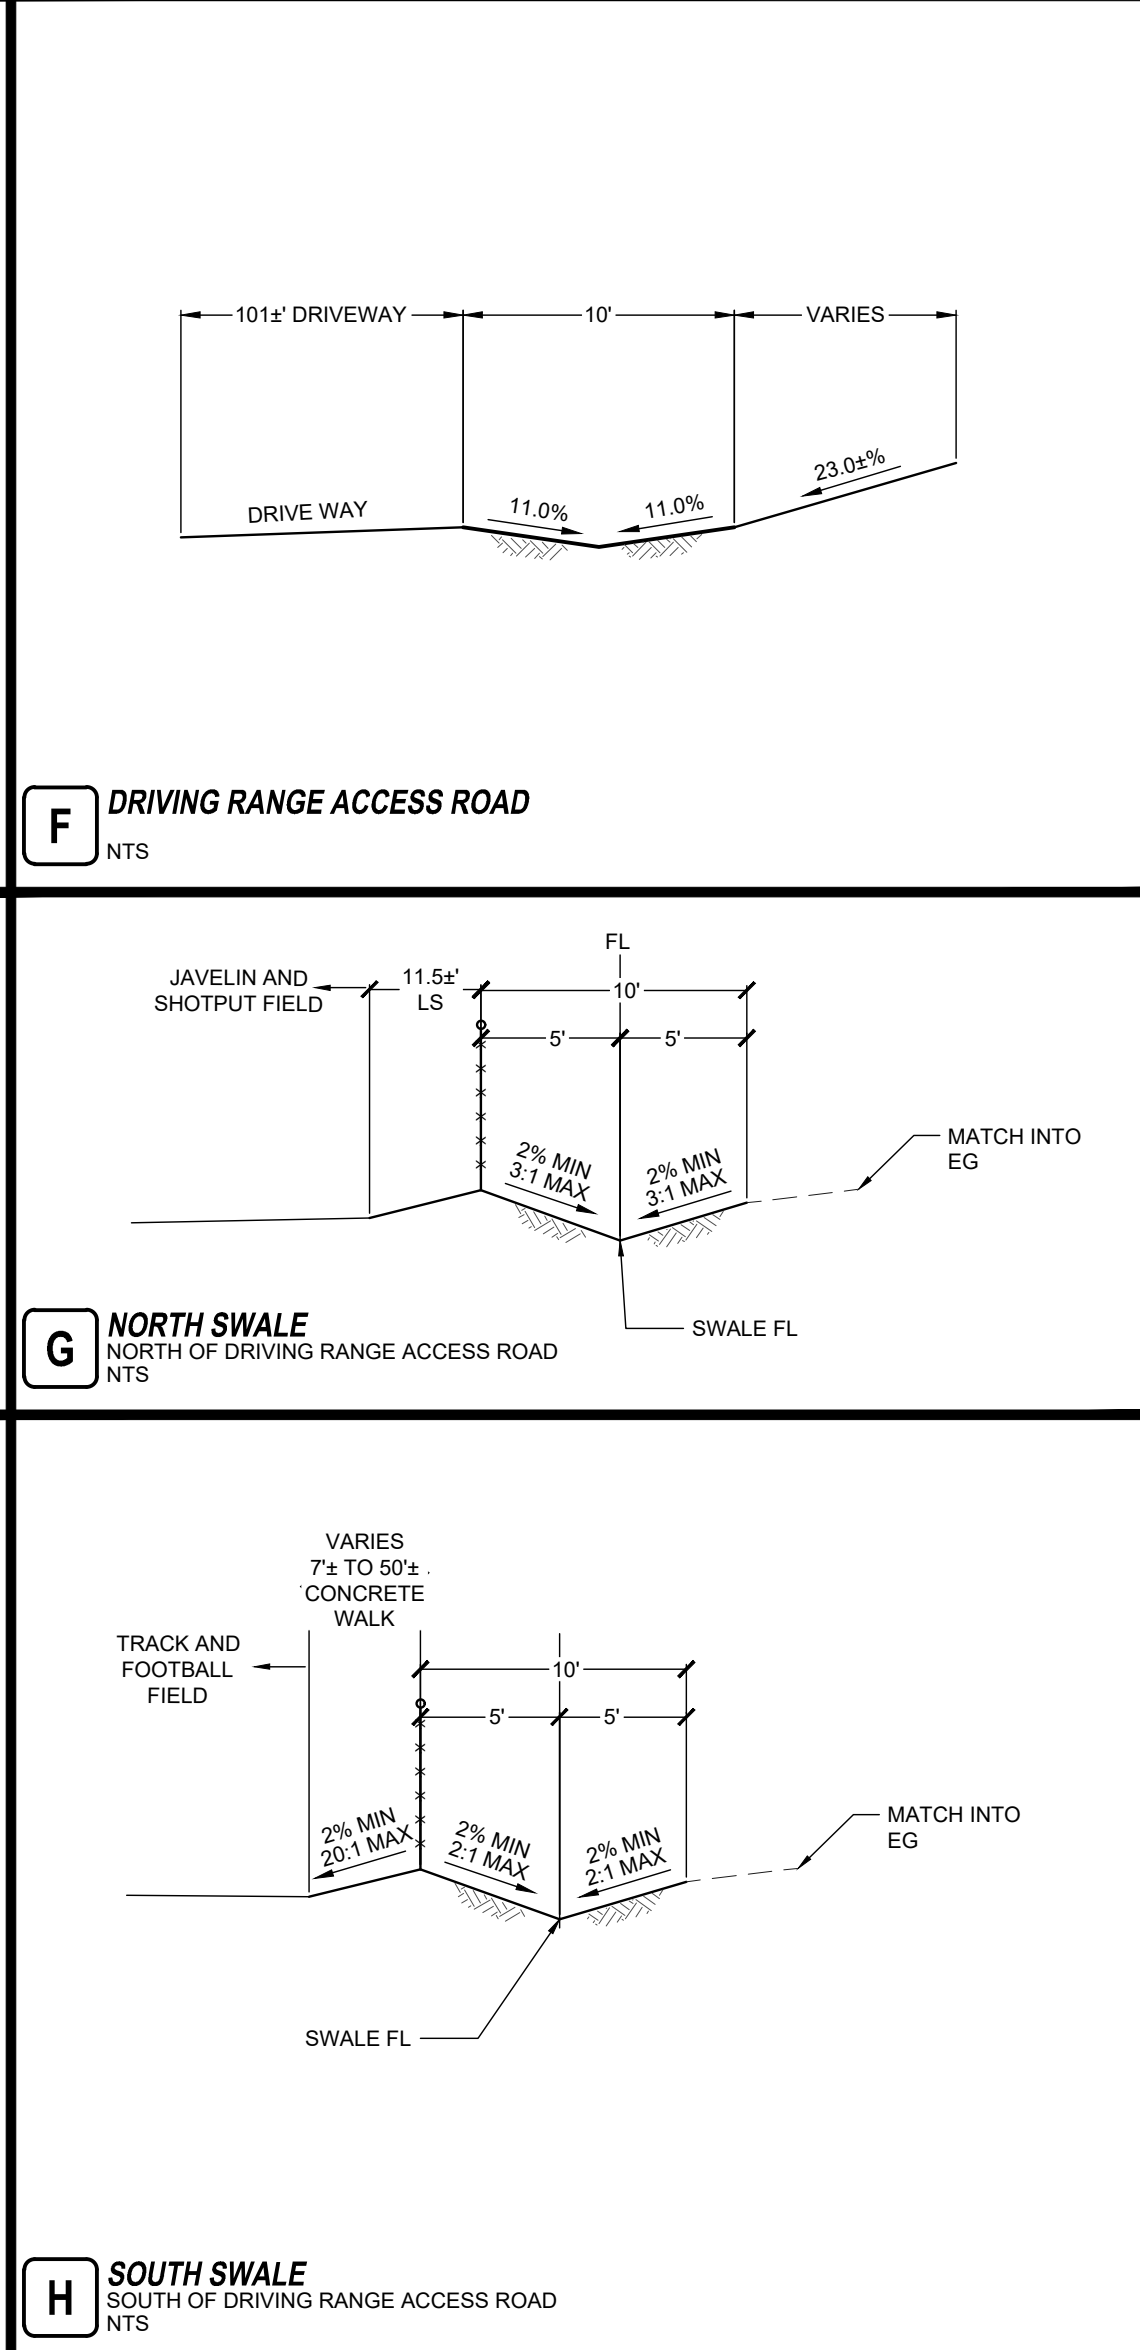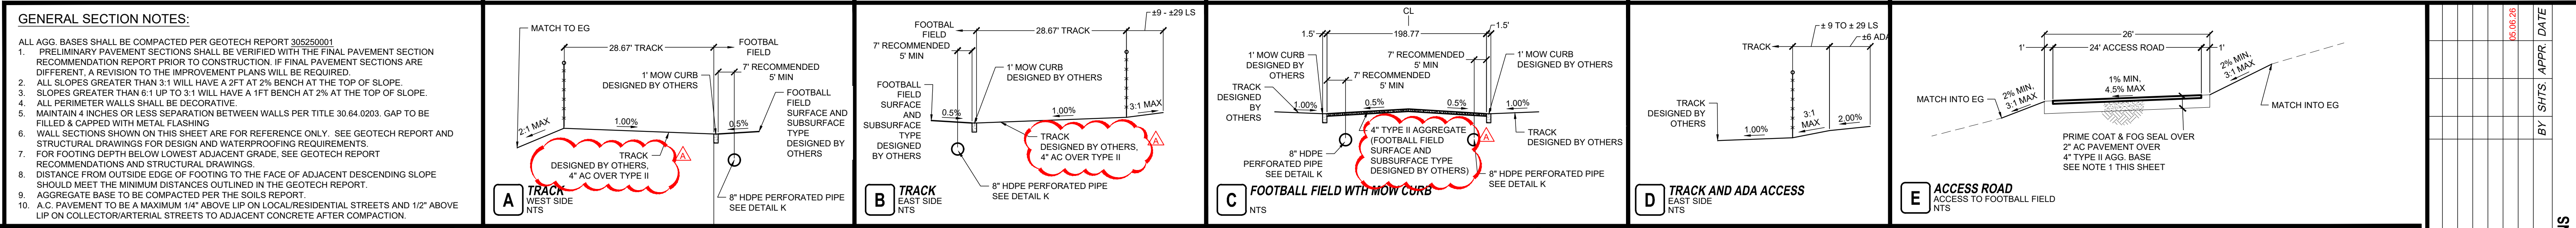

REVISIONS

NO	DESCRIPTION	BY	SHTS	APPR	DATE
1	ADDENDUM #1				05/06/2026

KNIT DESIGNING COMMUNITY

TANEY ENGINEERING
CIVIL ENGINEERING & LAND SURVEYING
6030 S. JONES BLVD
LAS VEGAS, NV 89118
(702) 362-8844
INFO@TANEYCORP.COM

TONOPAH HS FOOTBALL FIELD FOOTBALL FIELD NYE COUNTY SCHOOL DISTRICT

GRADING DETAILS

BRIAN E. MYERS
Exp. 12-31-27
CIVIL
No. 23550
05/06/2026

DATE: 5/6/2026
SCALE: NTS
JOB NO: KNC-24-009
DESIGNED BY: BS1 CHECKED BY: BM
SHEET NAME: GD
SHEET NUMBER: 07 OF 09
NYE 00000000

LAST PLOT: Plot Sheets
FILE NAME: S:\ACTIVENT DESIGNING COMMUNITIES\KNC-24-009 - TONOPAH SCHOOL - FOOTBALL FIELD\ENG3\IPSS3 SHEET DWG\KNC209_SHT_GD.DWG